专 业 SPECIALTY	签 名 SIGNATURE	日 期 DATE	专 业 SPECIALTY	签 名 SIGNATURE	日 期 DATE
建 筑 ARCHITECTURE			暖 通 MECHANICAL		
结 构 STRUCTURE			强 电 ELECTRICAL		
给排水 PLUMBING			弱 电 TELECOM		

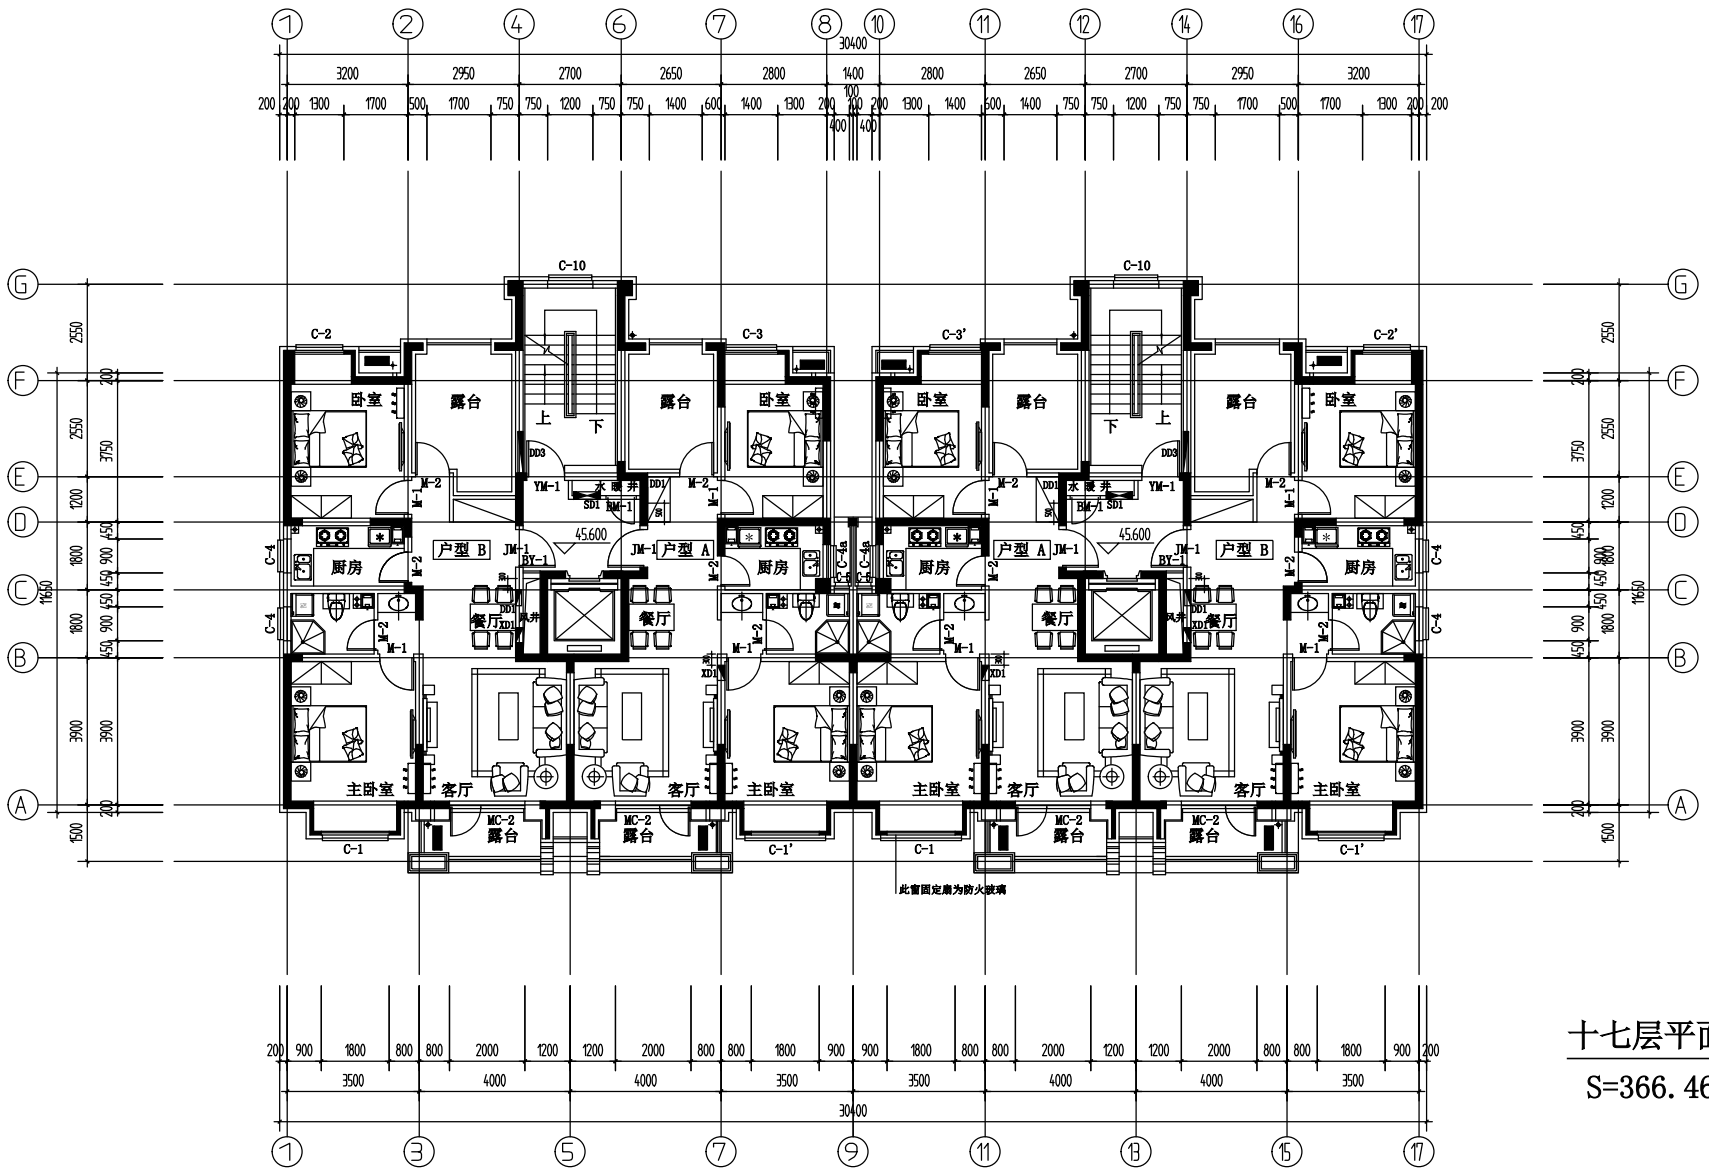

十七层平面图 1:100

S=366.46m²

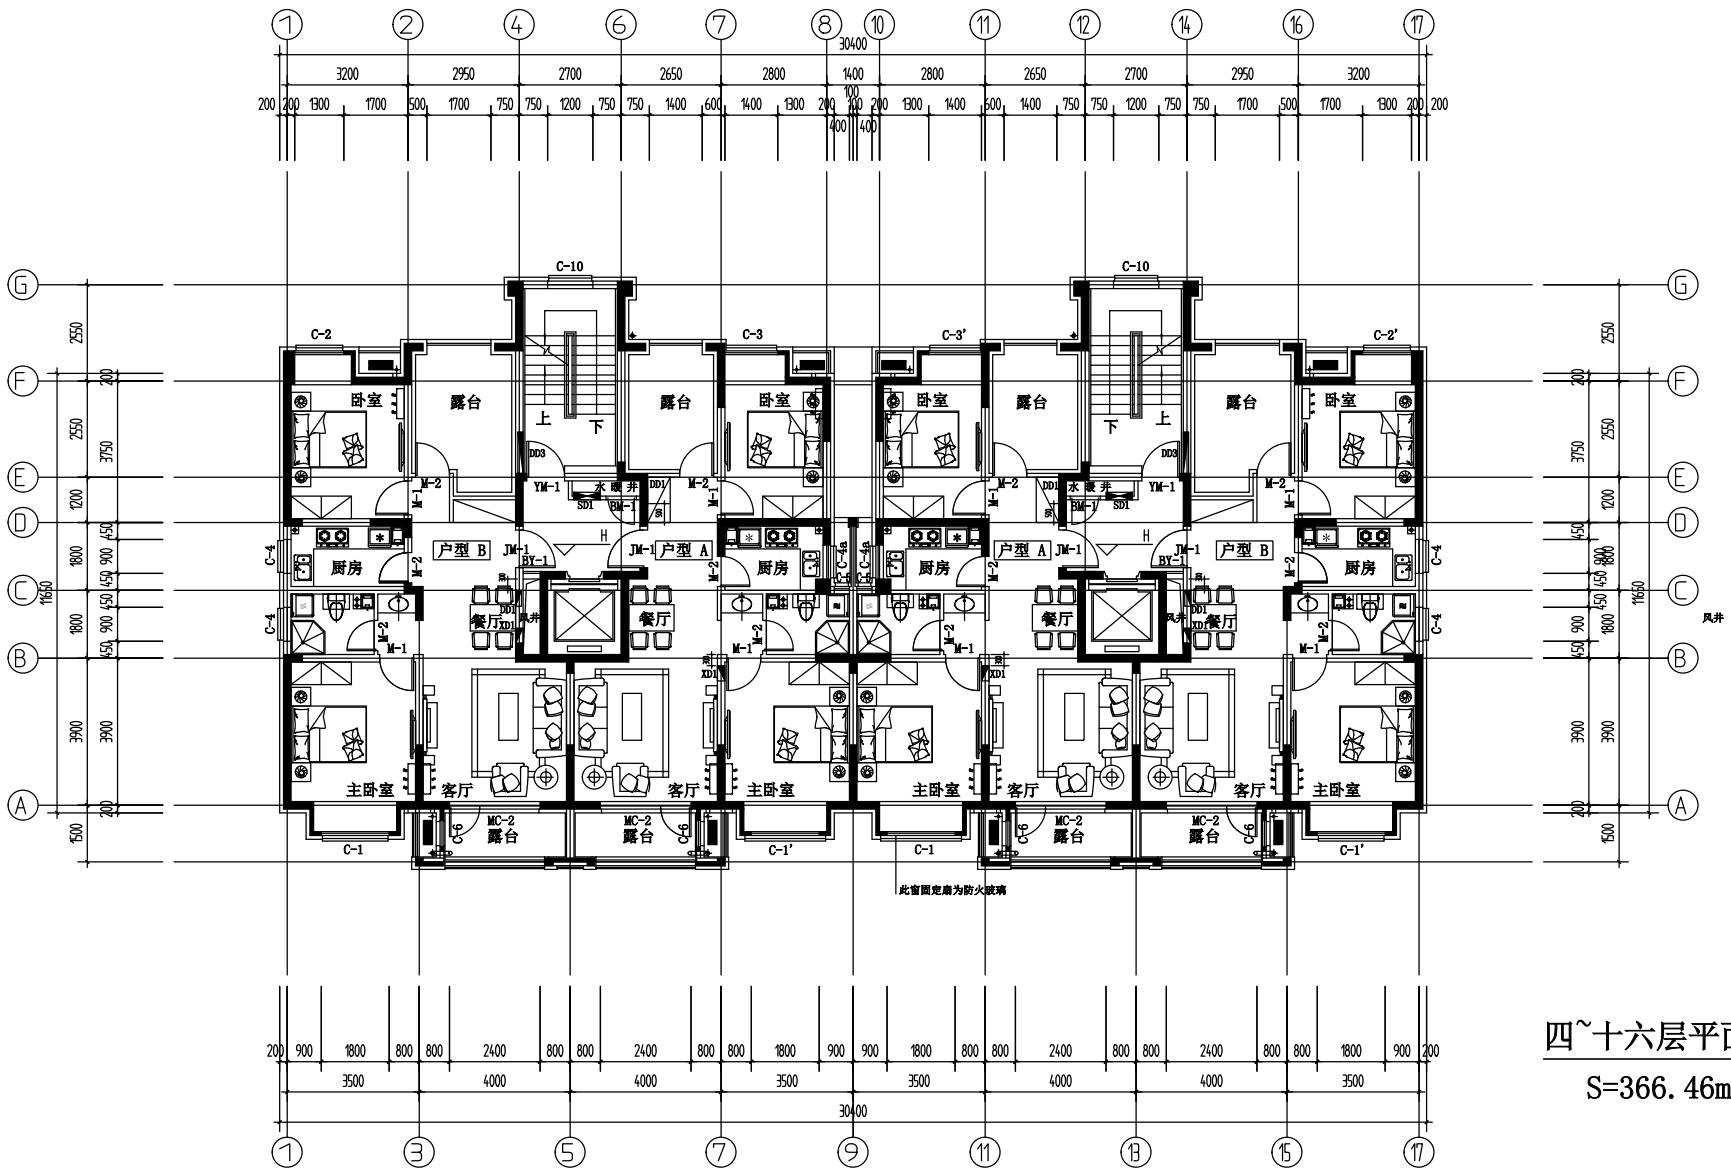

四~十六层平面图 1:100

S=366.46m²

25.650	
22.800	42.750
19.950	39.900
17.100	37.050
14.250	34.200
11.400	31.350
H= 8.550	28.500

中国中建设计集团有限公司
CHINA CONSTRUCTION ENGINEERING DESIGN GROUP CORPORATION LIMITED

工程设计甲级证书 A111007751
Architectural Design License No. A111007751
中国北京三里河路15号中建大厦(邮编 100037)
9F-A, CSEGD Mansion, NO. 15, Sanlihe Road, Beijing, China, 100037

合作方 PARTNERS

业务 STAMP

通用注释 GENERAL NOTES

1. 请勿量测图纸，所有尺寸以文字为准。
Do not scale drawings, all dimensions are as shown.
2. 施工前，所有尺寸须现场核实。
All dimensions shall be verified prior to construction.
3. 未经图纸会签审批程序主管部门审查批准的图纸文件均为无效。
The drawings will be effective upon the written verifications and approvals by the local authorities.

索引图 KEY PLAN

版 本 REV.	日 期 DATE
1	2011.08.26

建设单位 CLIENT

沈阳荣盛中天房地产开发有限公司

项目名称 PROJECT NAME	紫提东郡
子项名称 SUB PROJECT	C25~3地块(7#8#9#17#2#住楼
项目编号 PROJECT NO.	2010-SY-30
设计总负责人 PROJECT MANAGER	毛 广
审 APPROVED 定	刘芳敏
审 EXAMINED 核	郑祝华
专业负责人 DIVISION CHIEF	毛 广
校 CHECKED 对	王华威
设 DESIGNED 计	魏 君
日 期 DATE	2011.08.26
比 例 SCALE	1:100
图 CATEGORY 别	建施
图 DRAWING NO. 号	B03
图 名 DRAWING TITLE	十七层平面图 四~十六层平面图